


+/- 13.32 Acre Boundary Survey
Sec. 13, T5N, R5W,
I.M., Grady Co. OK.

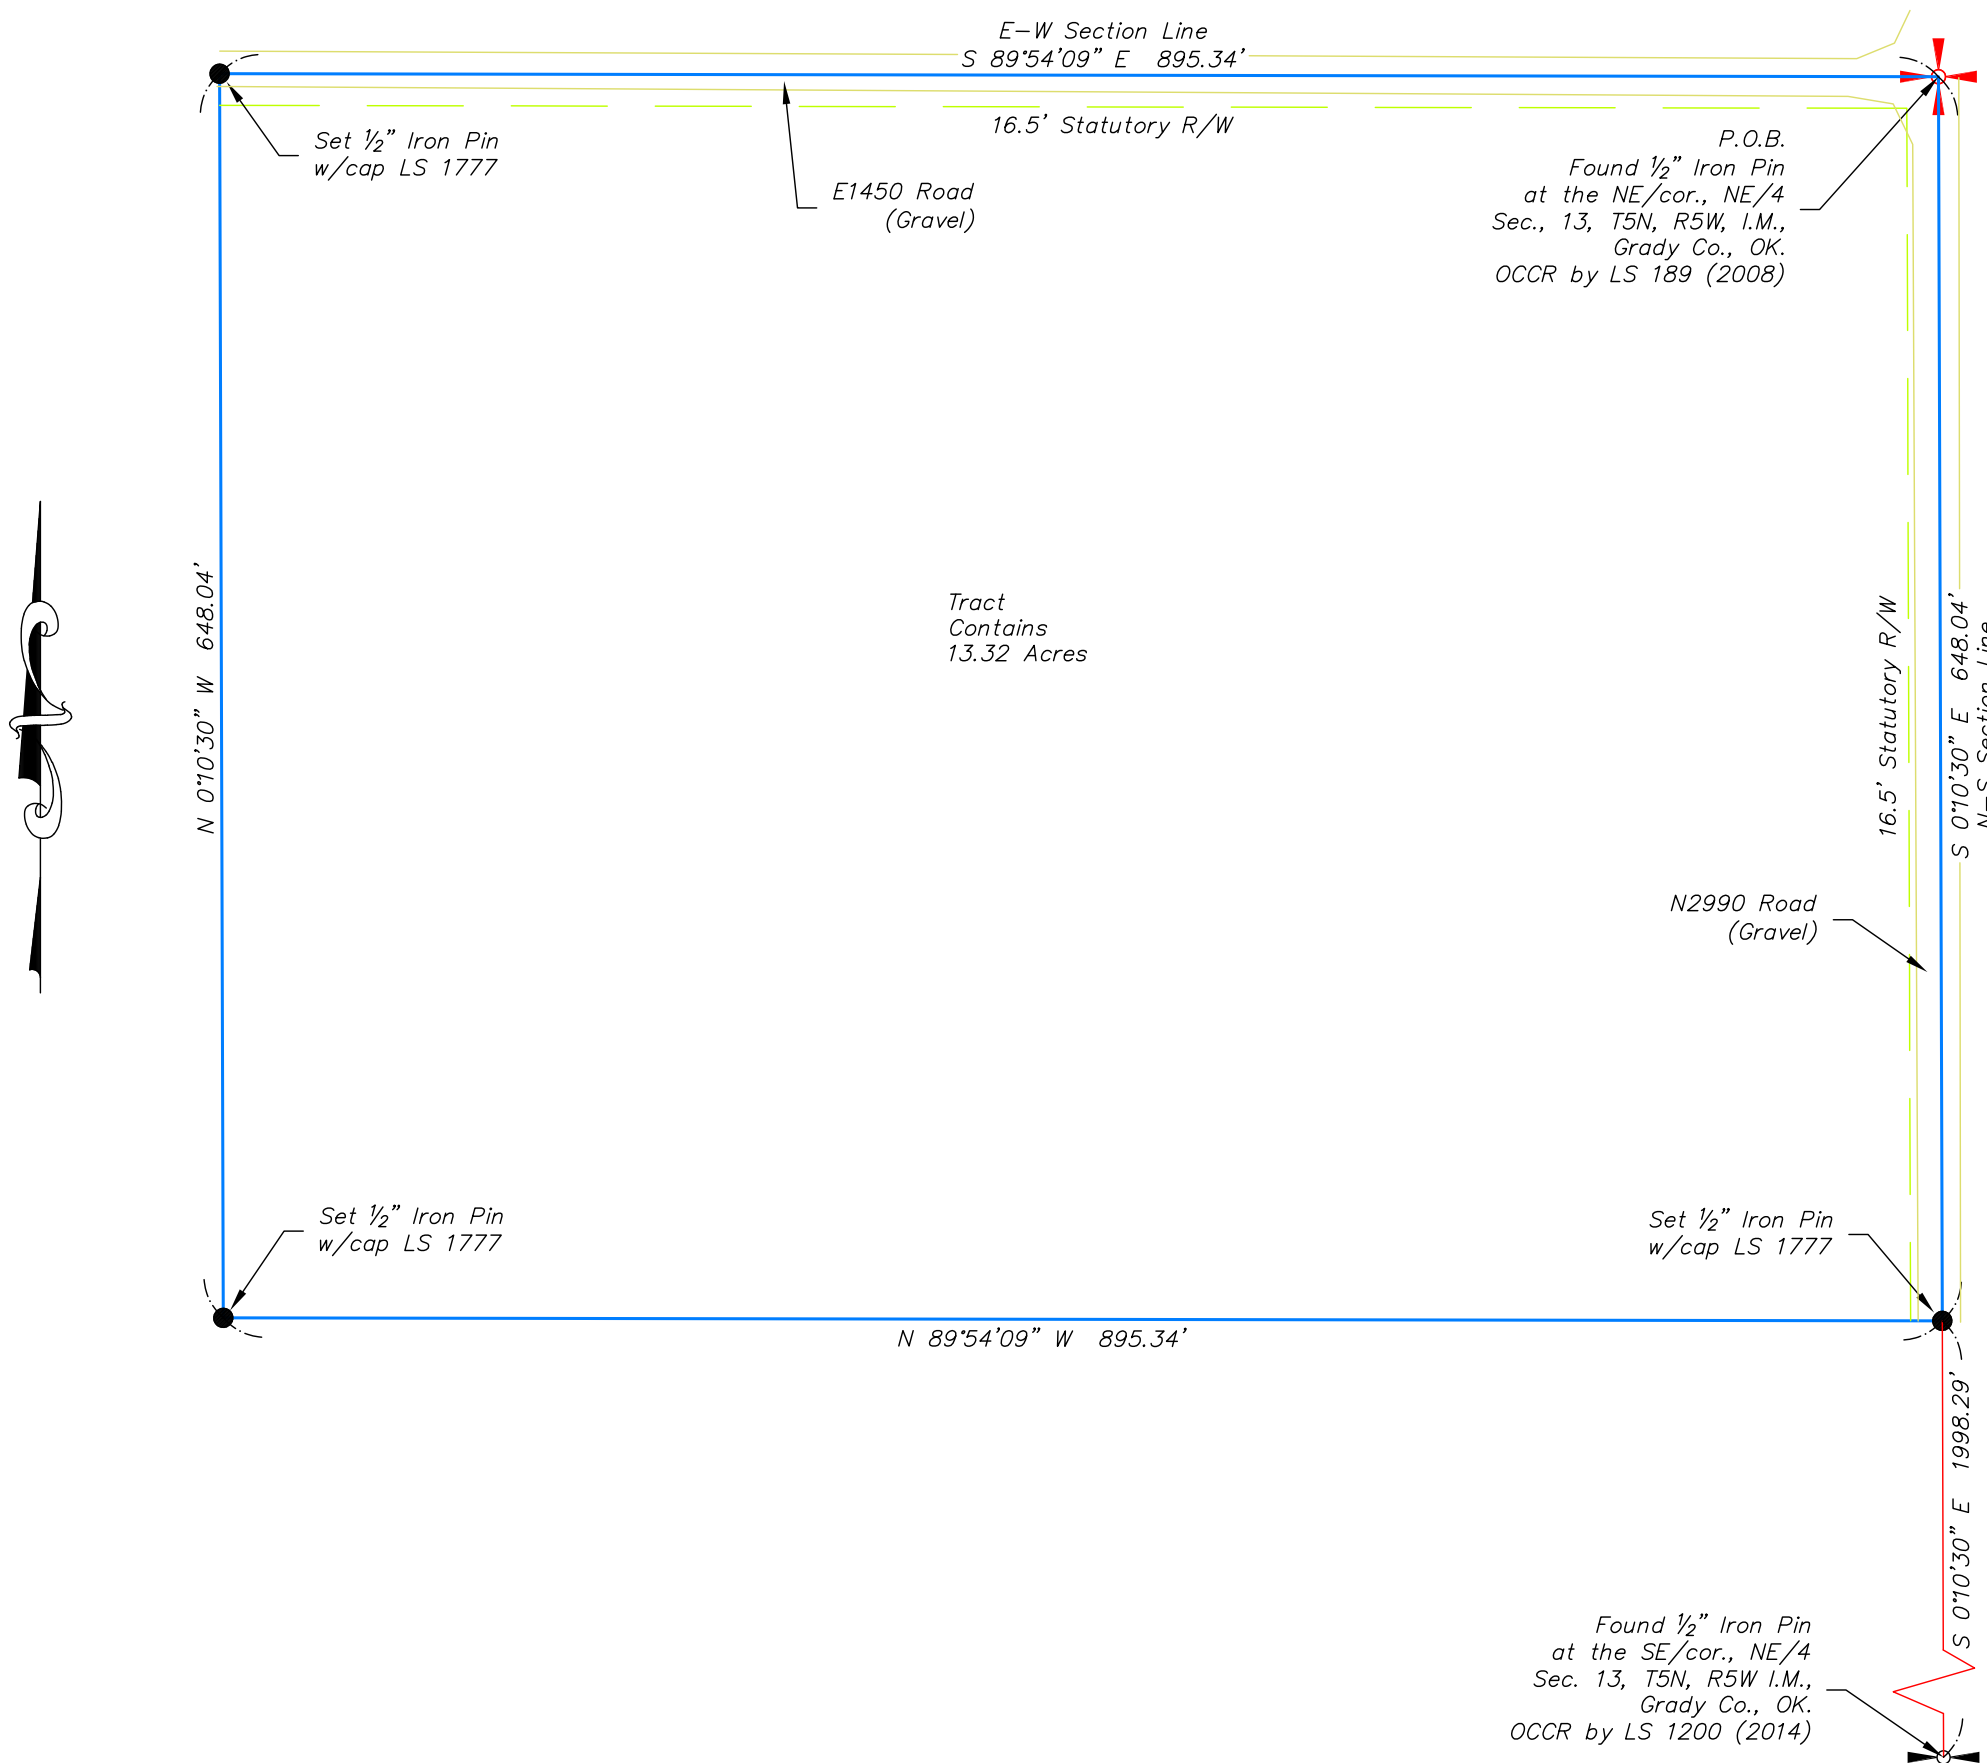

I, Clinton A. Carroll, A Licensed Professional Land Surveyor in the State of Oklahoma, do hereby certify that a careful survey has been made under my supervision of the above property described as follows:



13.32 Acre Tract Description:

A tract of land described as beginning at the Northeast corner of the Northeast Quarter of Section Thirteen (13), Township Five (5) North, Range Five (5) West, of the Indian Meridian in Grady County, Oklahoma;
Thence S 00°10'30" E, along the East line of said NE/4, a distance of 648.04 feet;
Thence N 89°54'09" W, parallel with the North line of said NE/4, a distance of 895.34 feet;
Thence N 00°10'30" W, parallel with the East line of said NE/4, a distance of 648.04 feet, said point being on the North line of said NE/4;
Thence S 89°54'09" E, along the North line of said NE/4, a distance of 895.34 feet to the point of beginning.
Said tract contains 13.32 acres of land, more or less.

Bearings for this description are grid and based on the Oklahoma State plane Coordinate System of 1983 South Zone, holding S 00°10'30" along the East line of the Northeast Quarter. This description was prepared on May 3, 2026 by Clinton A. Carroll, PLS 1777. Certificate of Authorization number 2706 expires June, 2026.

I further certify that this survey meets the Oklahoma Minimum Standards for the practice of land surveying and that there are no visible encroachments across the boundary lines other than those shown, and that the described property, as shown, is a true and accurate survey.

- Bearings and Distances are Grid and based on the Oklahoma South Coordinate System. (NAD83)
- All Angular and Distance Values SHOWN AS MEASURED on Survey Drawing unless otherwise noted
- Last Site Visit: April 30, 2026

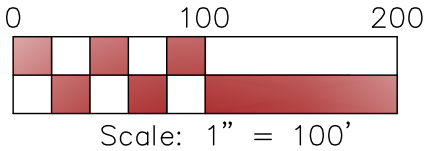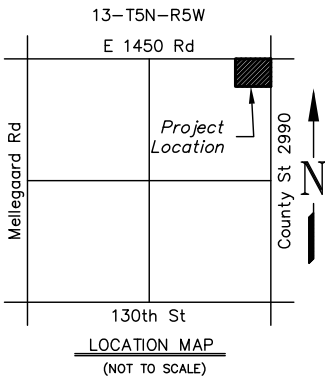

CARROLL SURVEYING & MAPPING

PO BOX 525
208 W. Choctaw St.
Marlow, OK 73055

Telephone: (580) 658-6405
Email: office@carrollsurveying.com
Certificate of Authortization# 2706