

+/- 32.72 Acre Boundary Survey
Sec. 13, T5N, R5W,
I.M., Grady Co. OK.

I, Clinton A. Carroll, A Licensed Professional Land Surveyor in the State of Oklahoma, do hereby certify that a careful survey has been made under my supervision of the above property described as follows:

32.72 Acre Tract Description:

A tract of land described as commencing at the Northeast corner of the Northeast Quarter of Section Thirteen (13), Township Five (5) North, Range Five (5) West, of the Indian Meridian in Grady County, Oklahoma;

Thence S 00°10'30" E, along the East line of said NE/4, a distance of 1432.80 feet to the point of beginning;

Thence continuing S 00°10'30" E, along the East line of the NE/4, a distance of 719.99 feet;

Thence N 89°50'40" W, parallel with the South line of said NE/4, a distance of 1982.84 feet, said point being on the West line of the E/2 W/2 E/2;





Thence N 00°06'57" W, along the West line of the E/2 W/2 E/2, a distance of 717.97 feet;

Thence S 89°54'09" E, parallel with the North line of said NE/4, a distance of 1982.09 feet to the point of beginning.

Said tract contains 32.72 acres of land, more or less.

Bearings for this description are grid and based on the Oklahoma State plane Coordinate System of 1983 South Zone, holding S 00°10'30" E along the East line of the Northeast Quarter. This description was prepared on May 3, 2026 by Clinton A. Carroll, PLS 1777. Certificate of Authorization number 2706 expires June, 2026.

I further certify that this survey meets the Oklahoma Minimum Standards for the practice of land surveying and that there are no visible encroachments across the boundary lines other than those shown, and that the described property, as shown, is a true and accurate survey.

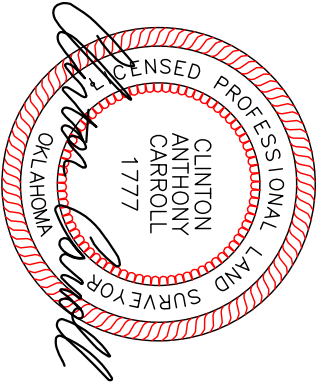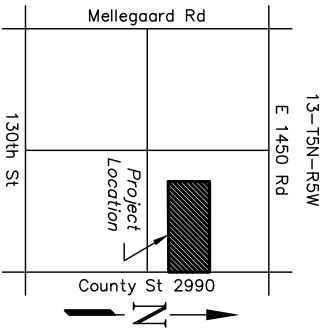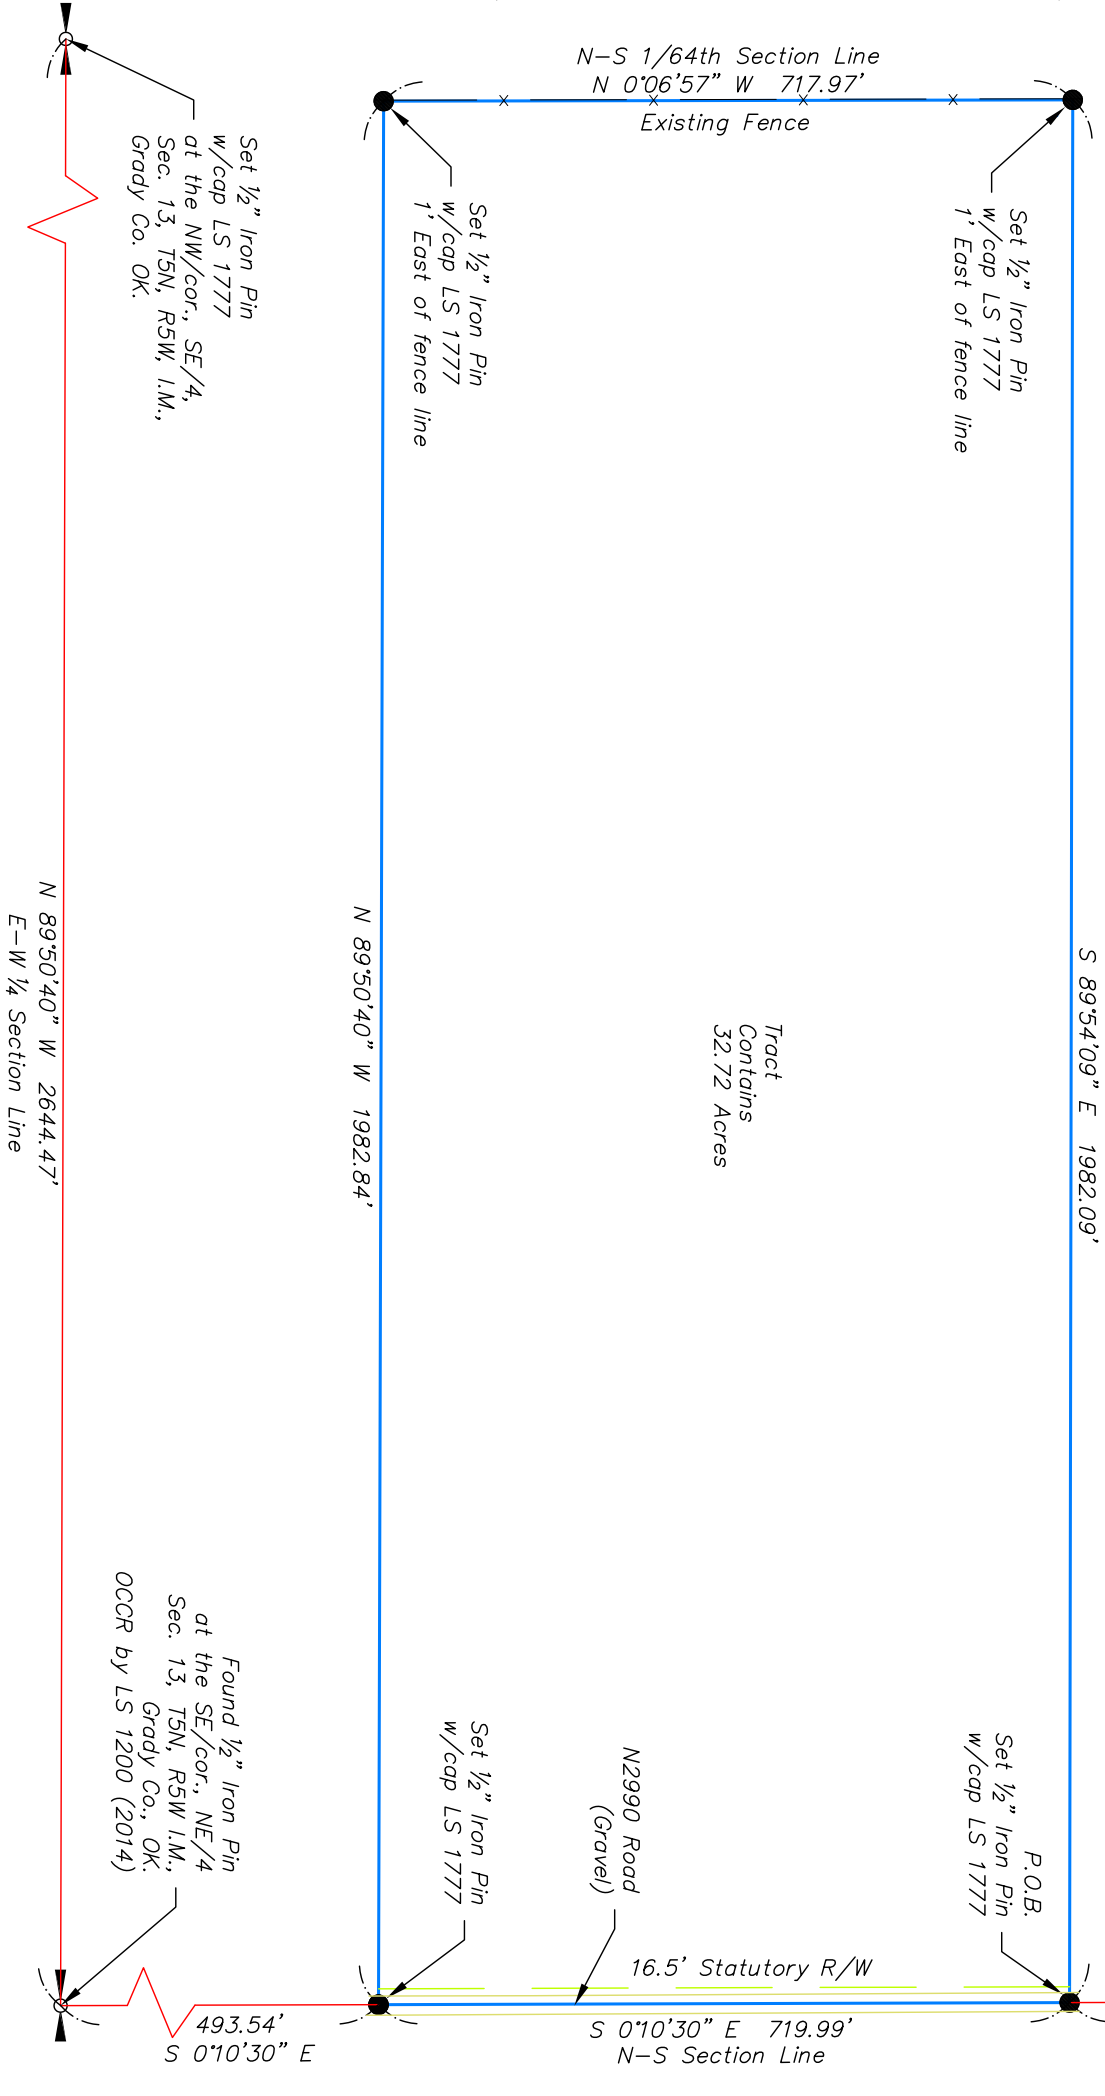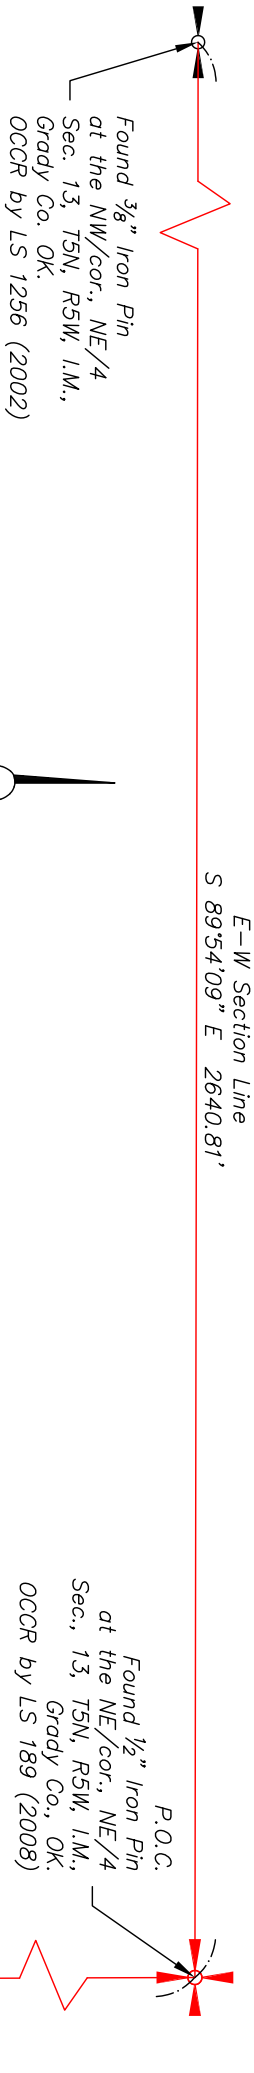

CARROLL SURVEYING & MAPPING

PO BOX 525
208 W. Choctaw St.
Marlow, OK 73055

Telephone: (580) 658-6405
Email: office@carrollsurveying.com
Certificate of Authorization# 2706