

+/- 16.15 Boundary Survey
Sec. 13, T5N, R5W,
I.M., Grady Co. OK.

P.O.C.
Found $\frac{3}{8}$ " Iron Pin
at the NW/cor., NE/4
Sec. 13, T5N, R5W, I.M.,
Grady Co., OK.
OCCR by LS 1256 (2002)


I, Clinton A. Carroll, A Licensed Professional Land Surveyor in the State of Oklahoma, do hereby certify that a careful survey has been made under my supervision of the above property described as follows:

16.15 Acre Tract Description:

A tract of land described as commencing at the Northwest corner of the Northeast Quarter of Section Thirteen (13), Township Five (5) North, Range Five (5) West, of the Indian Meridian in Grady County, Oklahoma;
Thence S 89°54'09" E, along the North line of said NE/4, a distance of 660.20 feet to the point of beginning, said point being the Northwest corner of the E/2 W/2 E/2;
Thence continuing S 89°54'09" E, along the North line of the NE/4, a distance of 1085.27 feet;
Thence S 00°10'30" E, parallel with the East line of said NE/4, a distance of 648.04 feet;
Thence N 89°54'09" W, parallel with the North line of said NE/4, a distance of 1085.94 feet, said point being on the West line of the E/2 W/2 E/2;
Thence N 00°06'57" W, along the West line of the E/2 W/2 E/2, a distance of 648.04 feet to the point of beginning.
Said tract contains 16.15 acres of land, more or less.

Bearings for this description are grid and based on the Oklahoma State plane Coordinate System of 1983 South Zone, holding S 89°54'09" E along the North line of the Northeast Quarter. This description was prepared on May 3, 2026 by Clinton A. Carroll, PLS 1777. Certificate of Authorization number 2706 expires June, 2026.

I further certify that this survey meets the Oklahoma Minimum Standards for the practice of land surveying and that there are no visible encroachments across the boundary lines other than those shown, and that the described property, as shown, is a true and accurate survey.

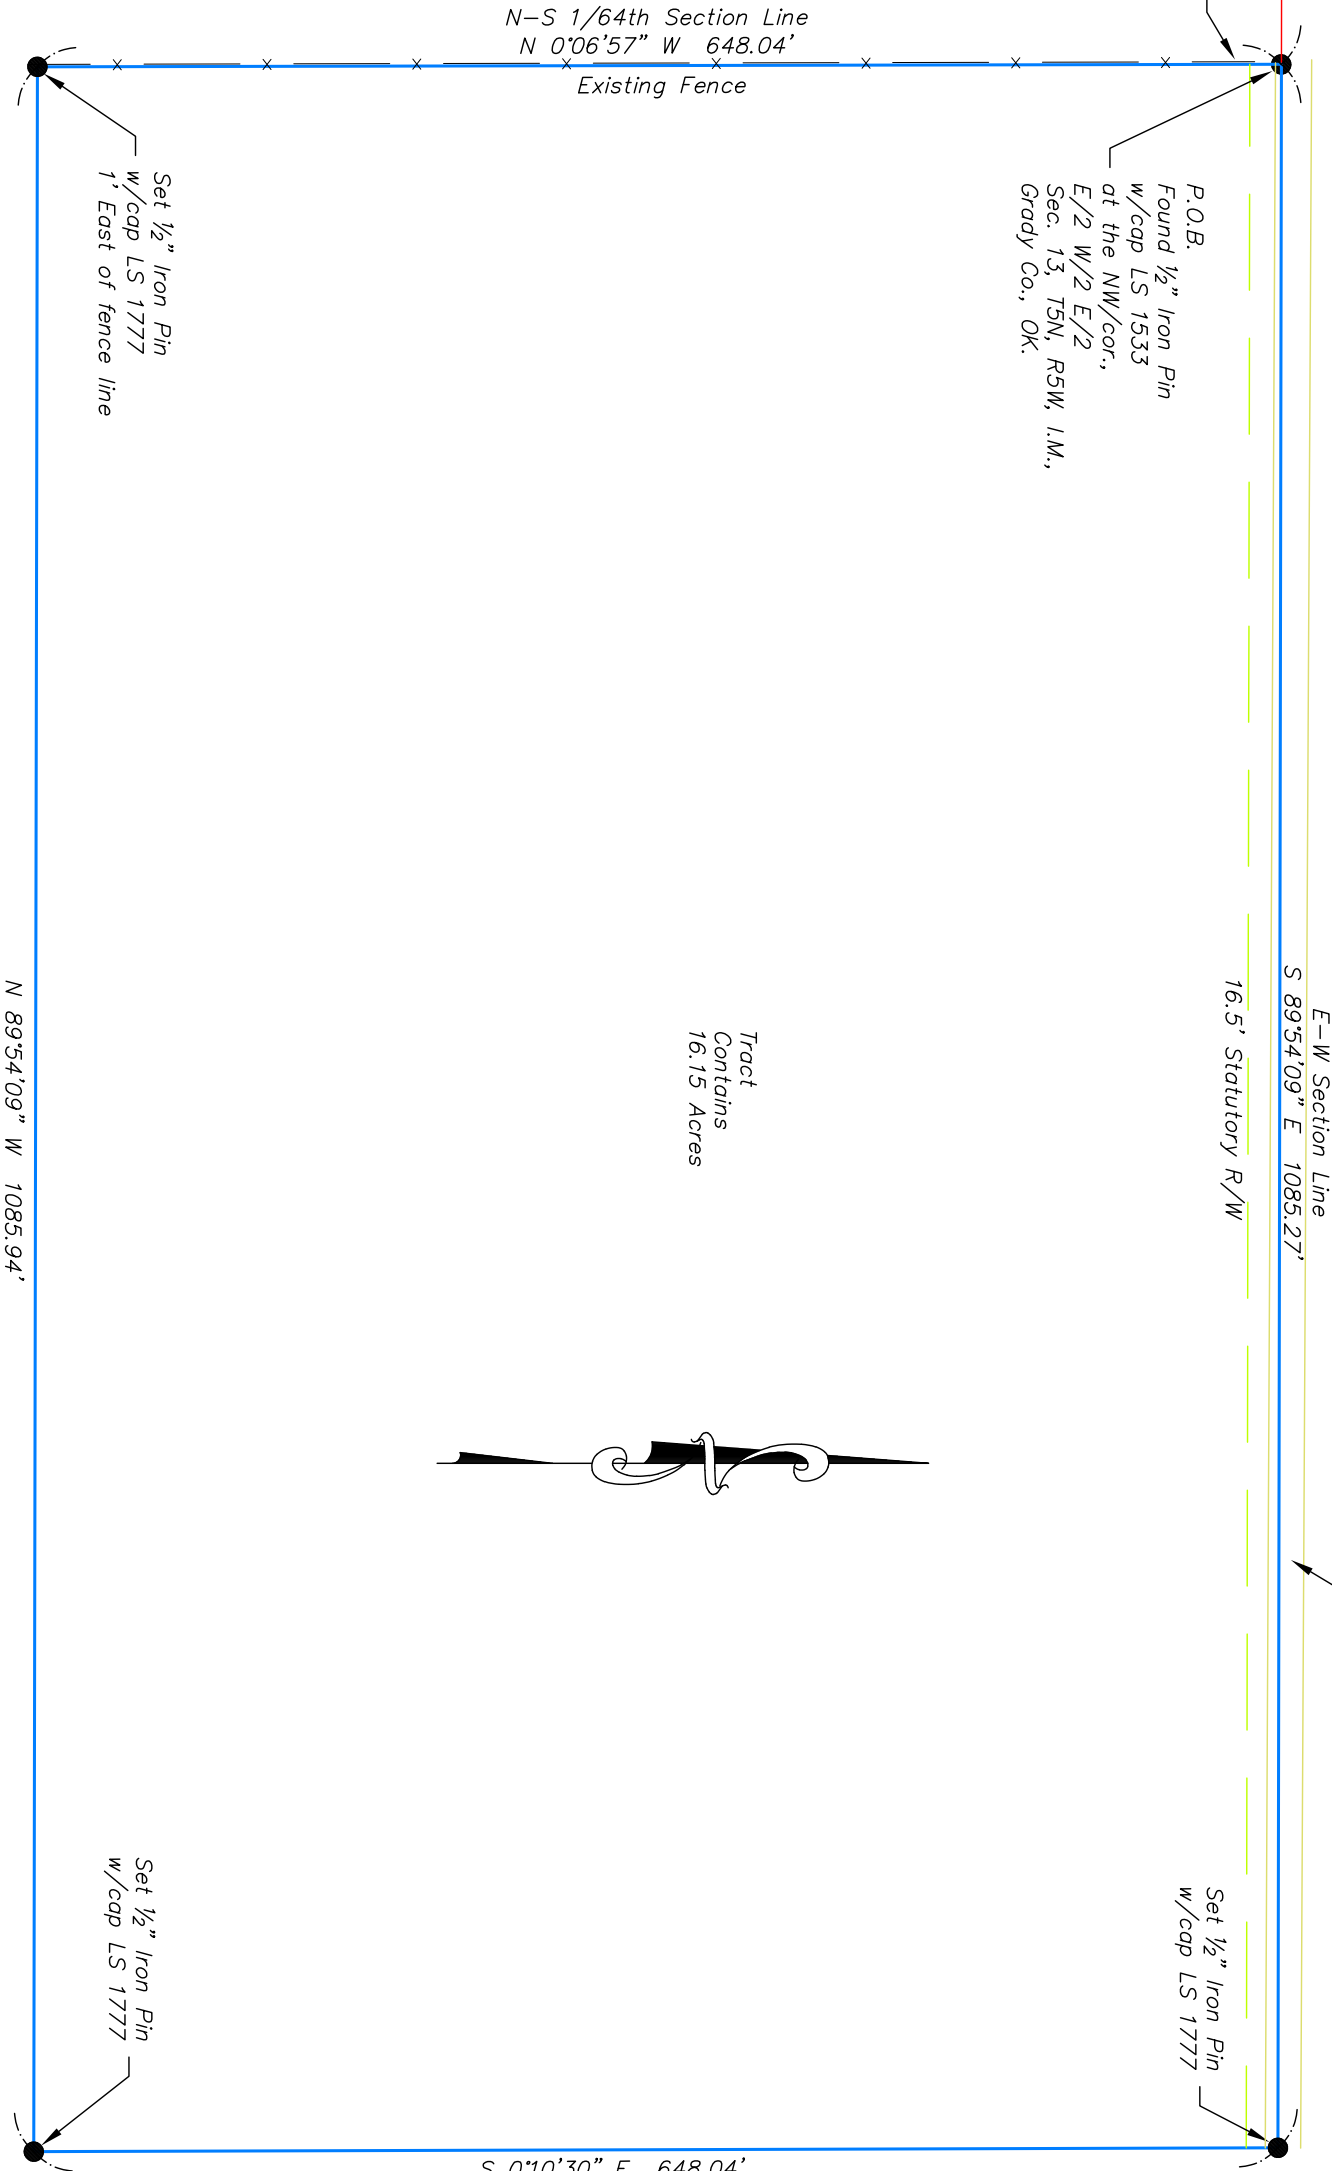

Fence is
1' West

P.O.B.
Found $\frac{1}{2}$ " Iron Pin
w/cap LS 1533
at the NW/cor.,
E/2 W/2 E/2
Sec. 13, T5N, R5W, I.M.,
Grady Co., OK.

E-W Section Line

S 89°54'09" E 1085.27'

16.5' Statutory R/W

E1450 Road
(Gravel)

Set $\frac{1}{2}$ " Iron Pin
w/cap LS 1777

Tract
Contains
16.15 Acres



N-S 1/64th Section Line
N 0°06'57" W 648.04'

Existing Fence

Set $\frac{1}{2}$ " Iron Pin
w/cap LS 1777
1' East of fence line

N 89°54'09" W 1085.94'

S 0°10'30" E 648.04'

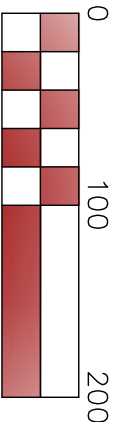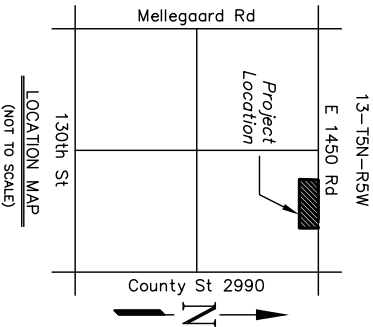

- Bearings and Distances are Grid and based on the Oklahoma South Coordinate System. (NAD83)
- All Angular and Distance Values SHOWN AS MEASURED on Survey Drawing unless otherwise noted
- Last Site Visit: April 30, 2026

