


Original Tract
Sec. 13, T5N, R5W,
I.M., Grady Co. OK.

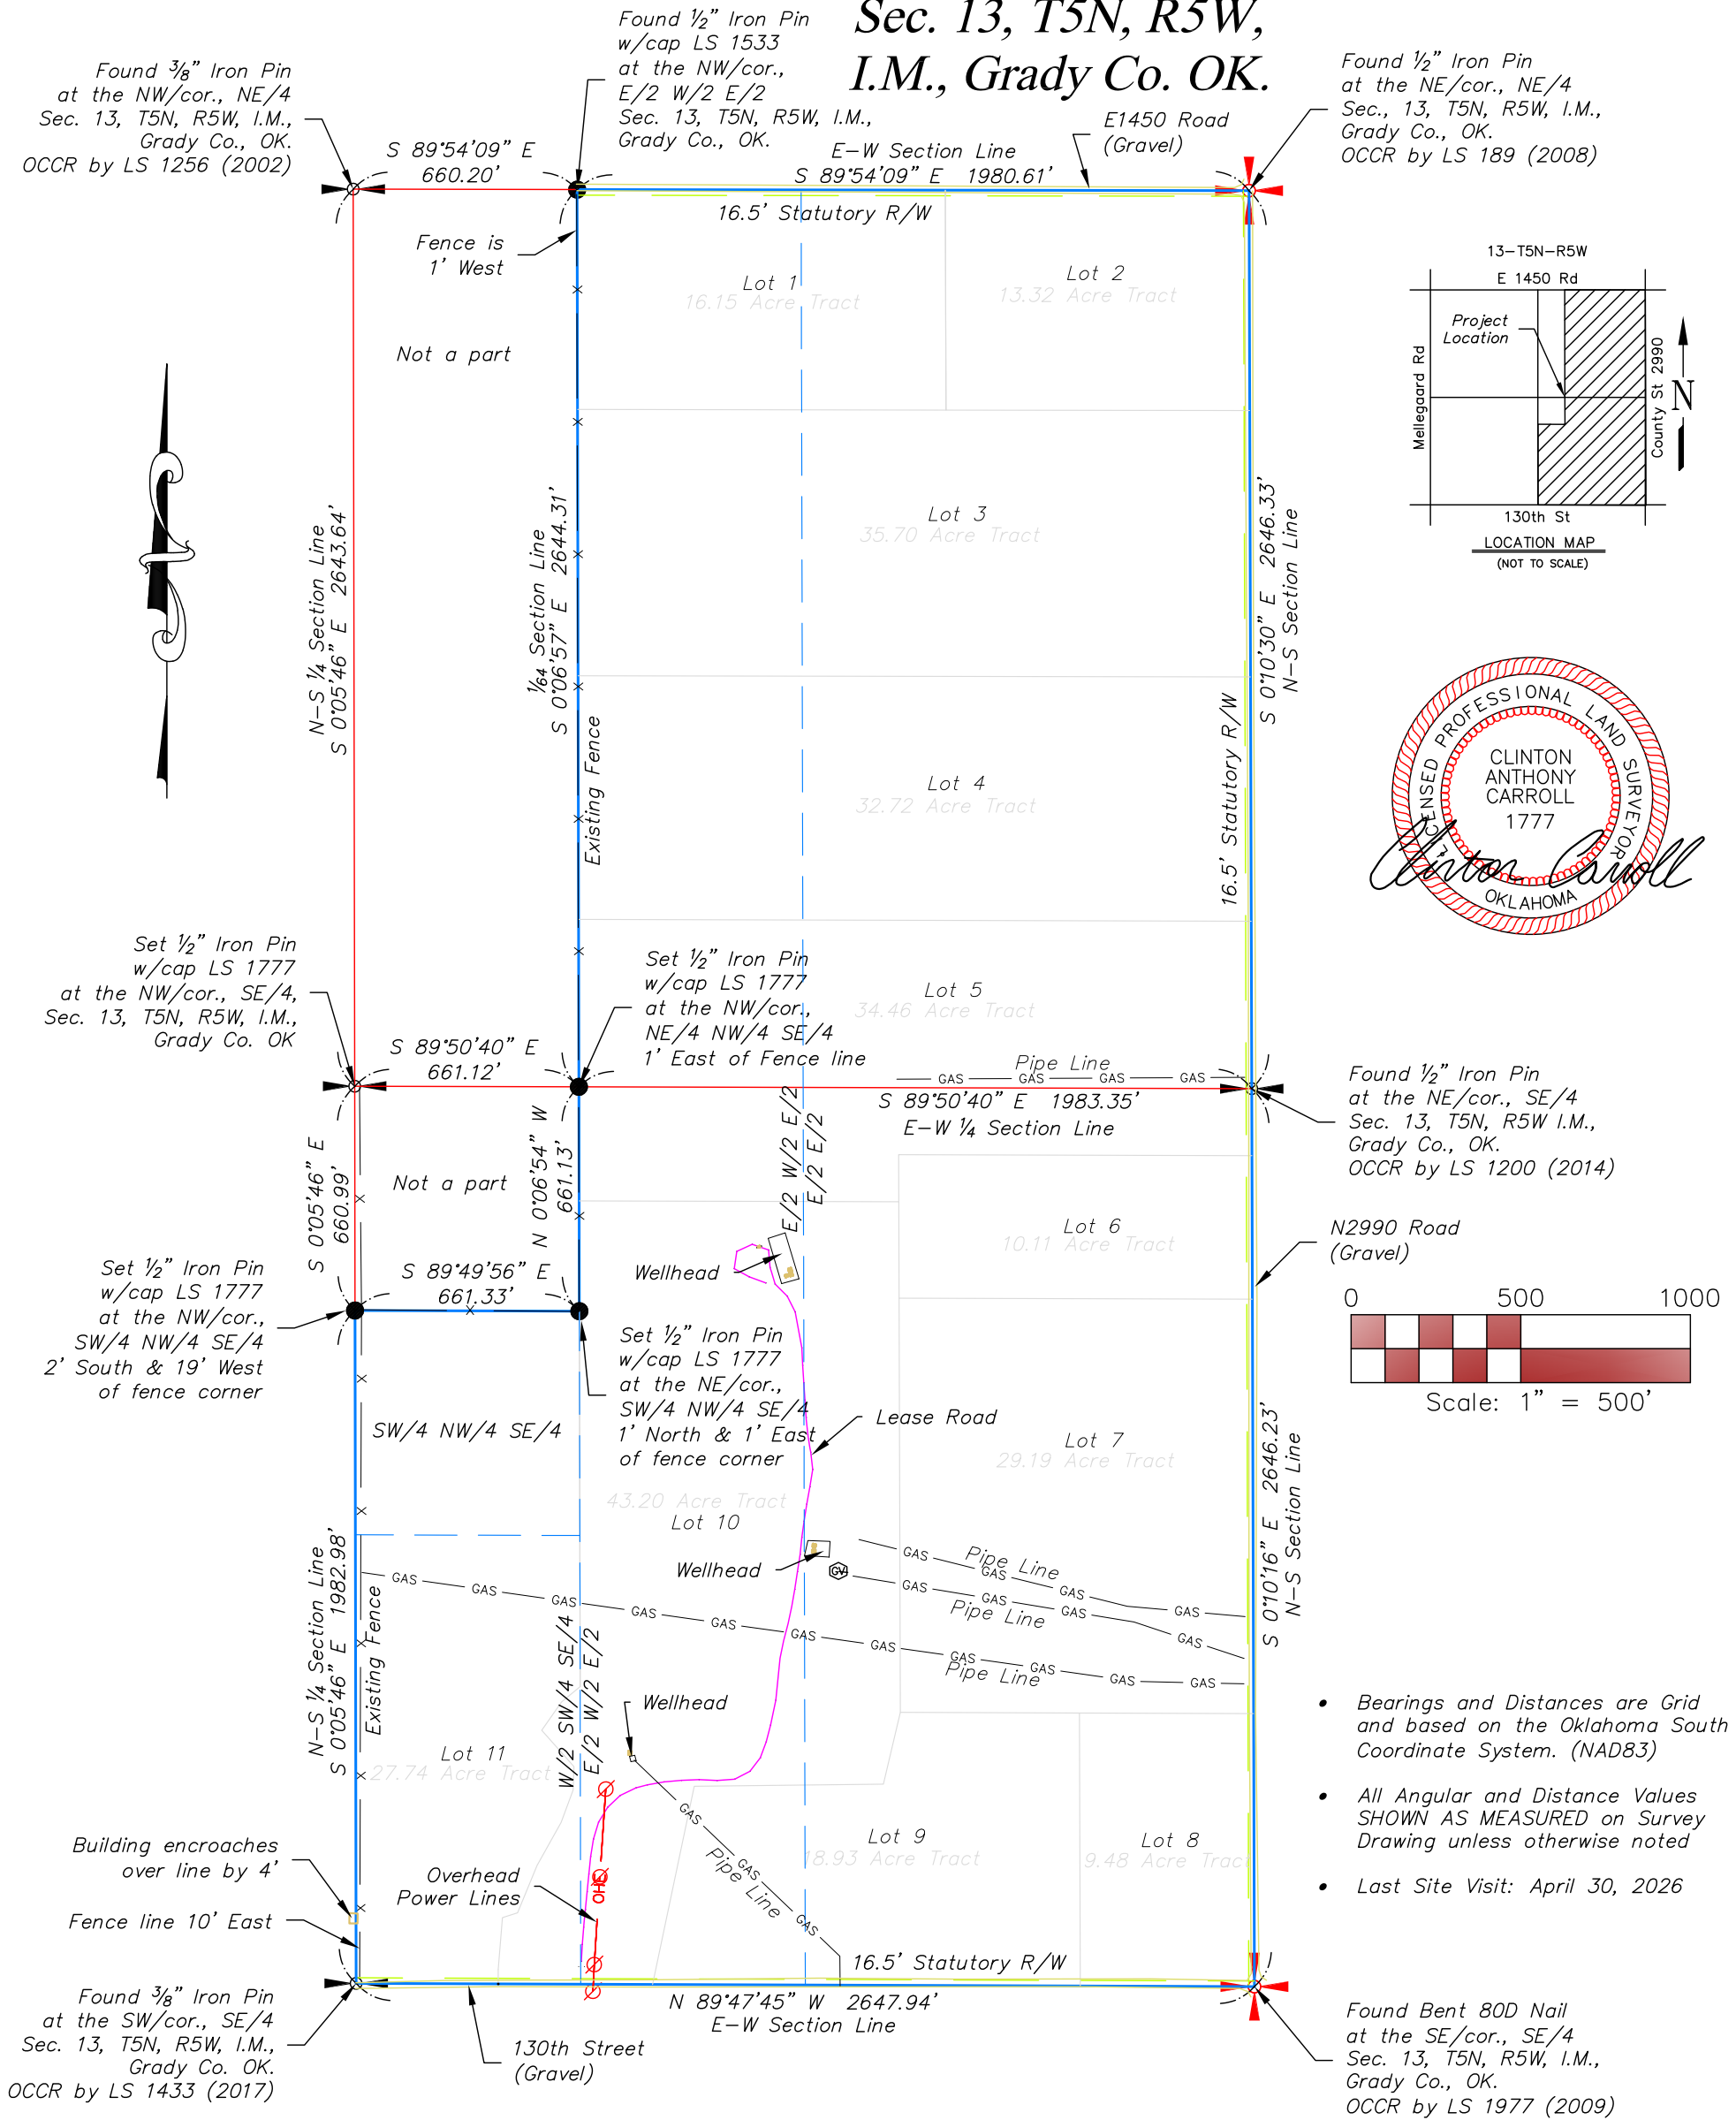

I, Clinton A. Carroll, A Licensed Professional Land Surveyor in the State of Oklahoma, do hereby certify that a careful survey has been made under my supervision of the above property described as follows:

Original Description filed in book 3055 page 472 at the Grady County Clerk's Office:

A tract of land described as the South half of the Southeast Quarter of the East half of the East half (E/2 E/2) and the East half of the West half of the East half (E/2 W/2 E/2) and the Southwest Quarter of the Northwest Quarter of the Southeast Quarter (SW/4 NW/4 SE/4) and the West half of the Southwest Quarter of the Southeast Quarter (W/2 SW/4 SE/4) in Section Thirteen (13), Township Five (5) North, Range Five (5) West, of the Indian Meridian in Grady County, Oklahoma;

Said tract contains 271.00 acres of land, more or less.

This description was prepared on May 3, 2026 by Clinton A. Carroll, PLS 1777. Certificate of Authorization number 2706 expires June, 2026.

I further certify that this survey meets the Oklahoma Minimum Standards for the practice of land surveying and that there are no visible encroachments across the boundary lines other than those shown, and that the described property, as shown, is a true and accurate survey.